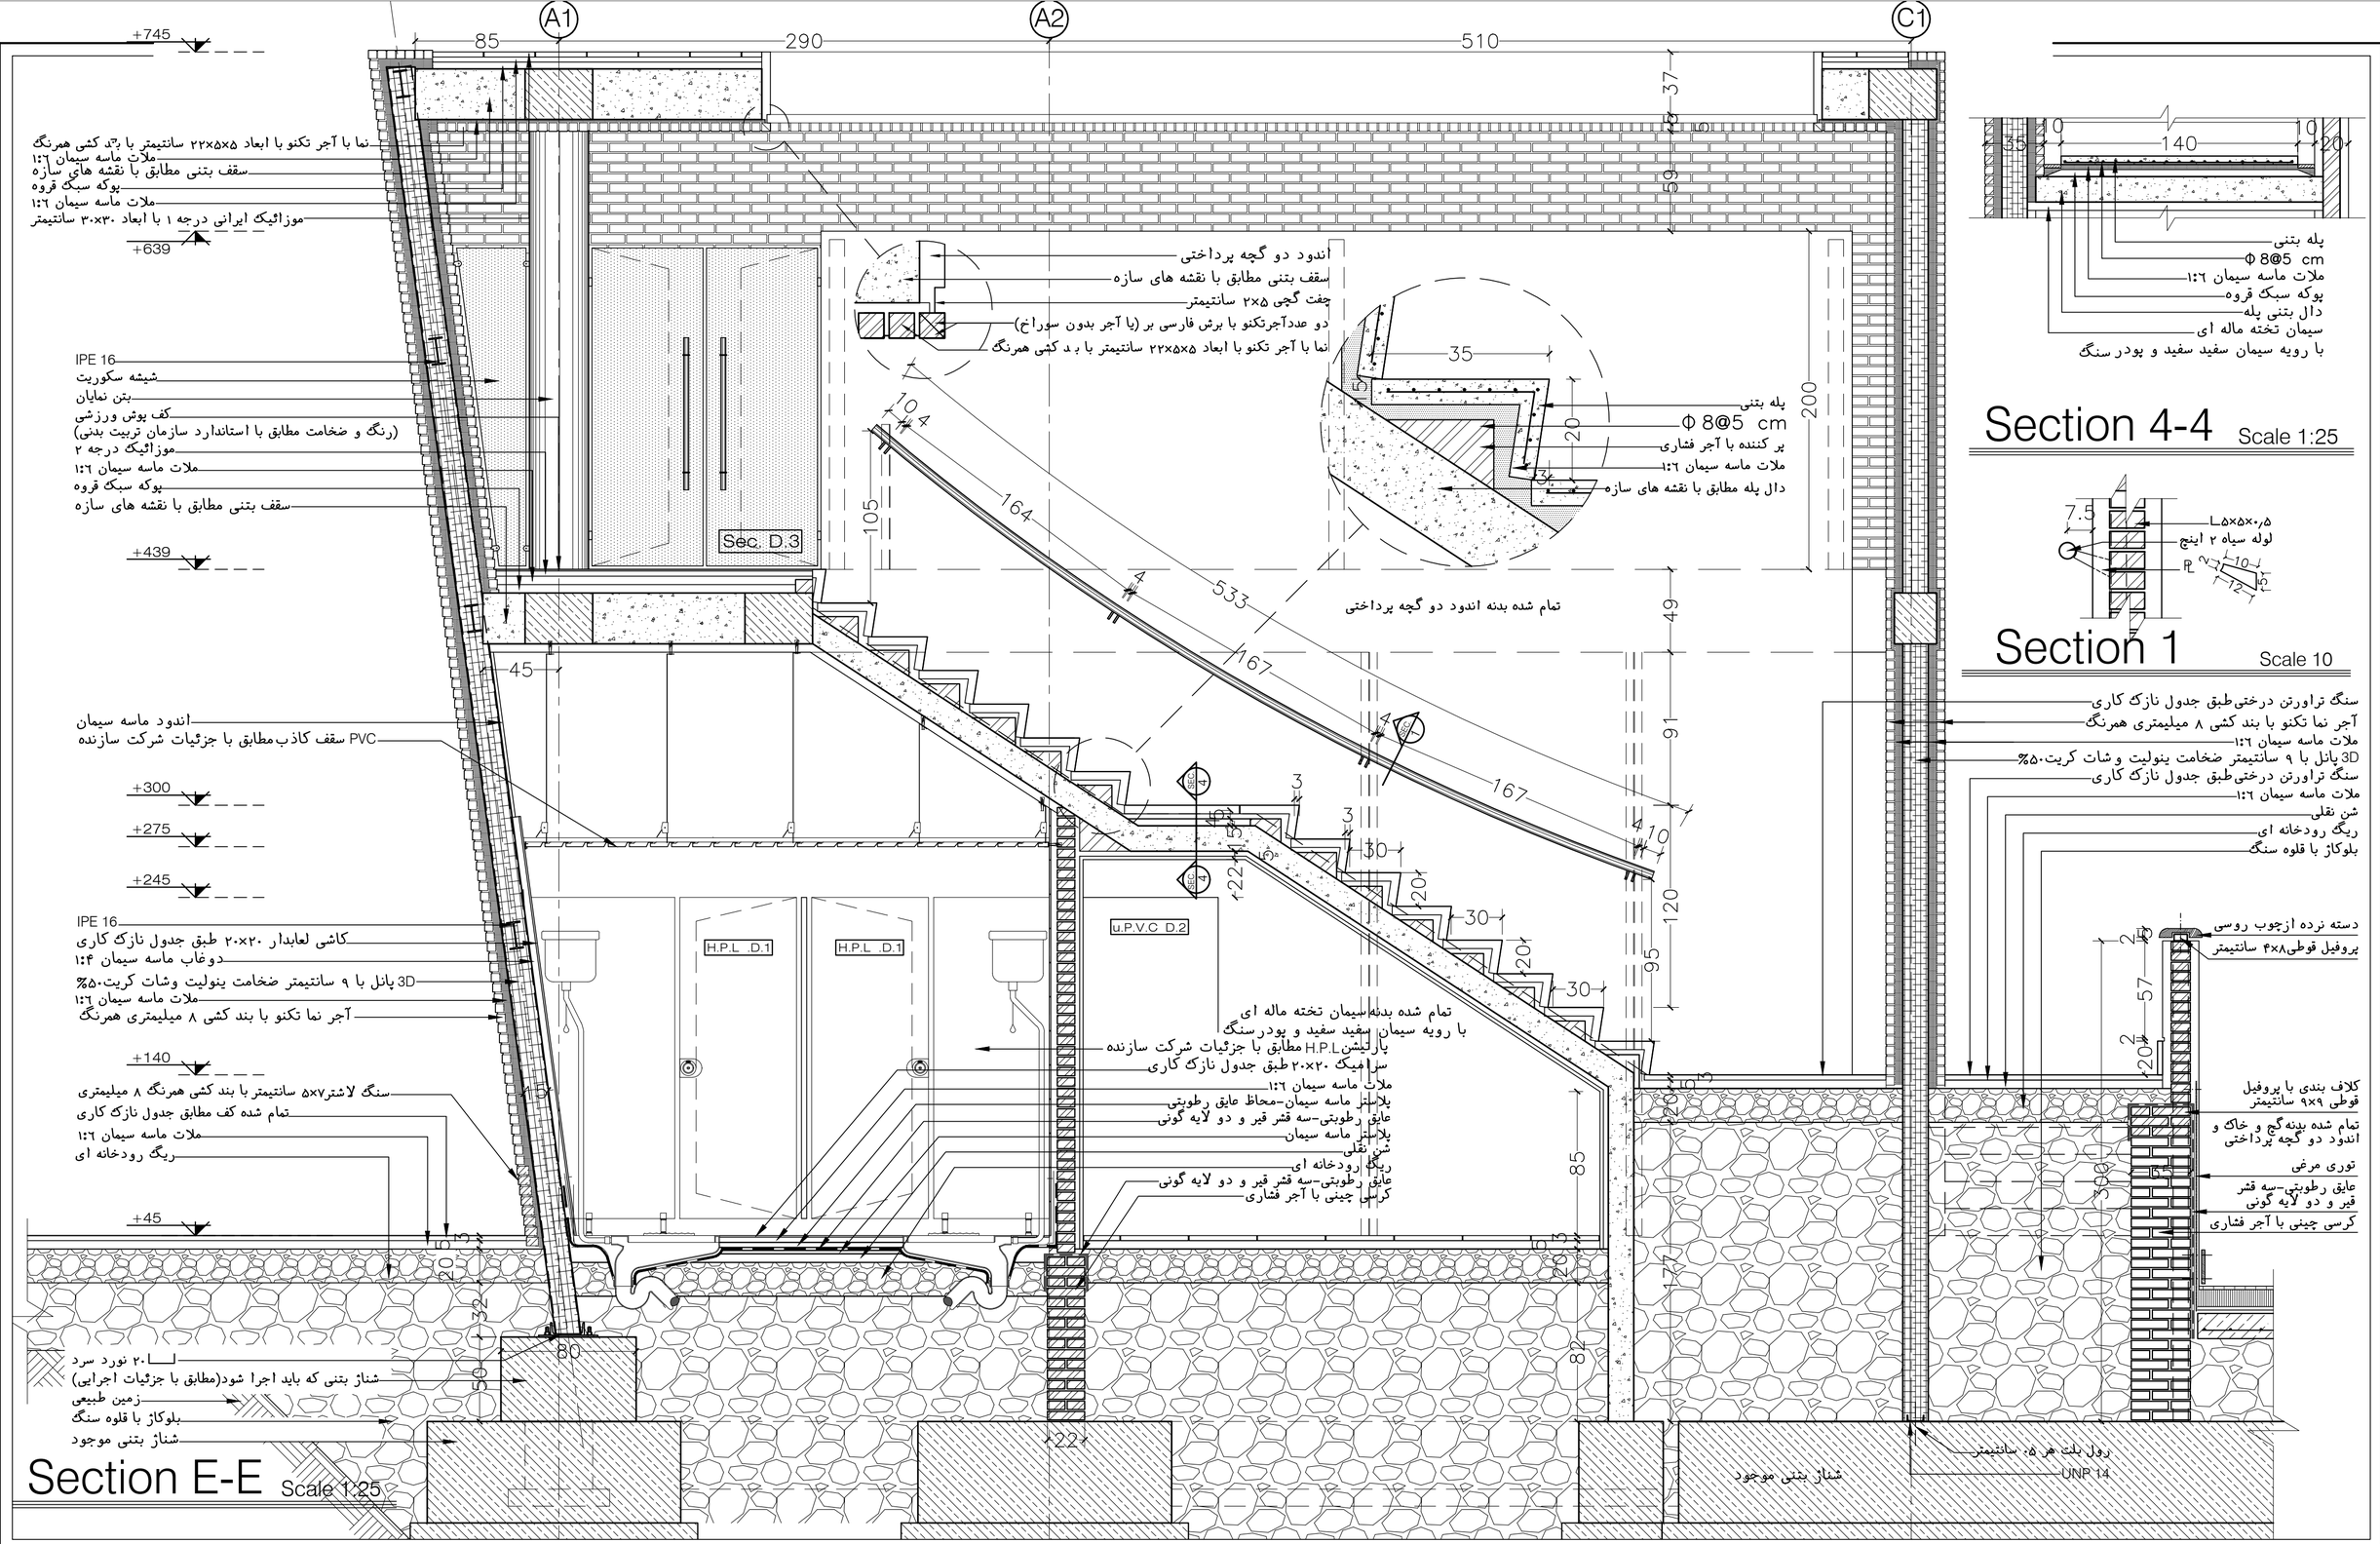

راهنمای نقشه

تغییرات:			
Rev.			
شماره:	تاریخ:	توضیحات:	تصویب:

شرکت آب منطقه‌ای استان اصفهان

کارفرما: شرکت آب منطقه ای استان اصفهان

Client:

Des. by:	طراح: ا - حیدری
Dwg. by:	ترسیم: ح - دانش
Chk. by:	کنترل: م - شرکت
Apr. by:	تصویب: ا - حیدری

Project Title:	نام پروژه: سالن ورزشی آبشار		
Sheet Title:	عنوان نقشه: بزرگنمایی ستگاه پله برش E-E		
Scale: 1/25	مقیاس:	Date: بهار ۹۰	Field: رشته: معماری
Dwg. No. 00 00 00 AR 14	شماره نقشه		Unit: واحد: سانتیمتر

DELTA
CONSULTANT ENGINEERS
Architects,Planners&Engineers
مهندسان مشاور دلتا